Жилой Дом Проба

Расшифровка ID :
МД1...МД5 - номер модуля
БЛ1 - Балки горизонтальные нижние
БЛ2 - Балки горизонтальные верхние
СТ - Балки вертикальные
ДСК - Доски 45х195 под балки обвязка
БР - Брусок 45х45 под балки

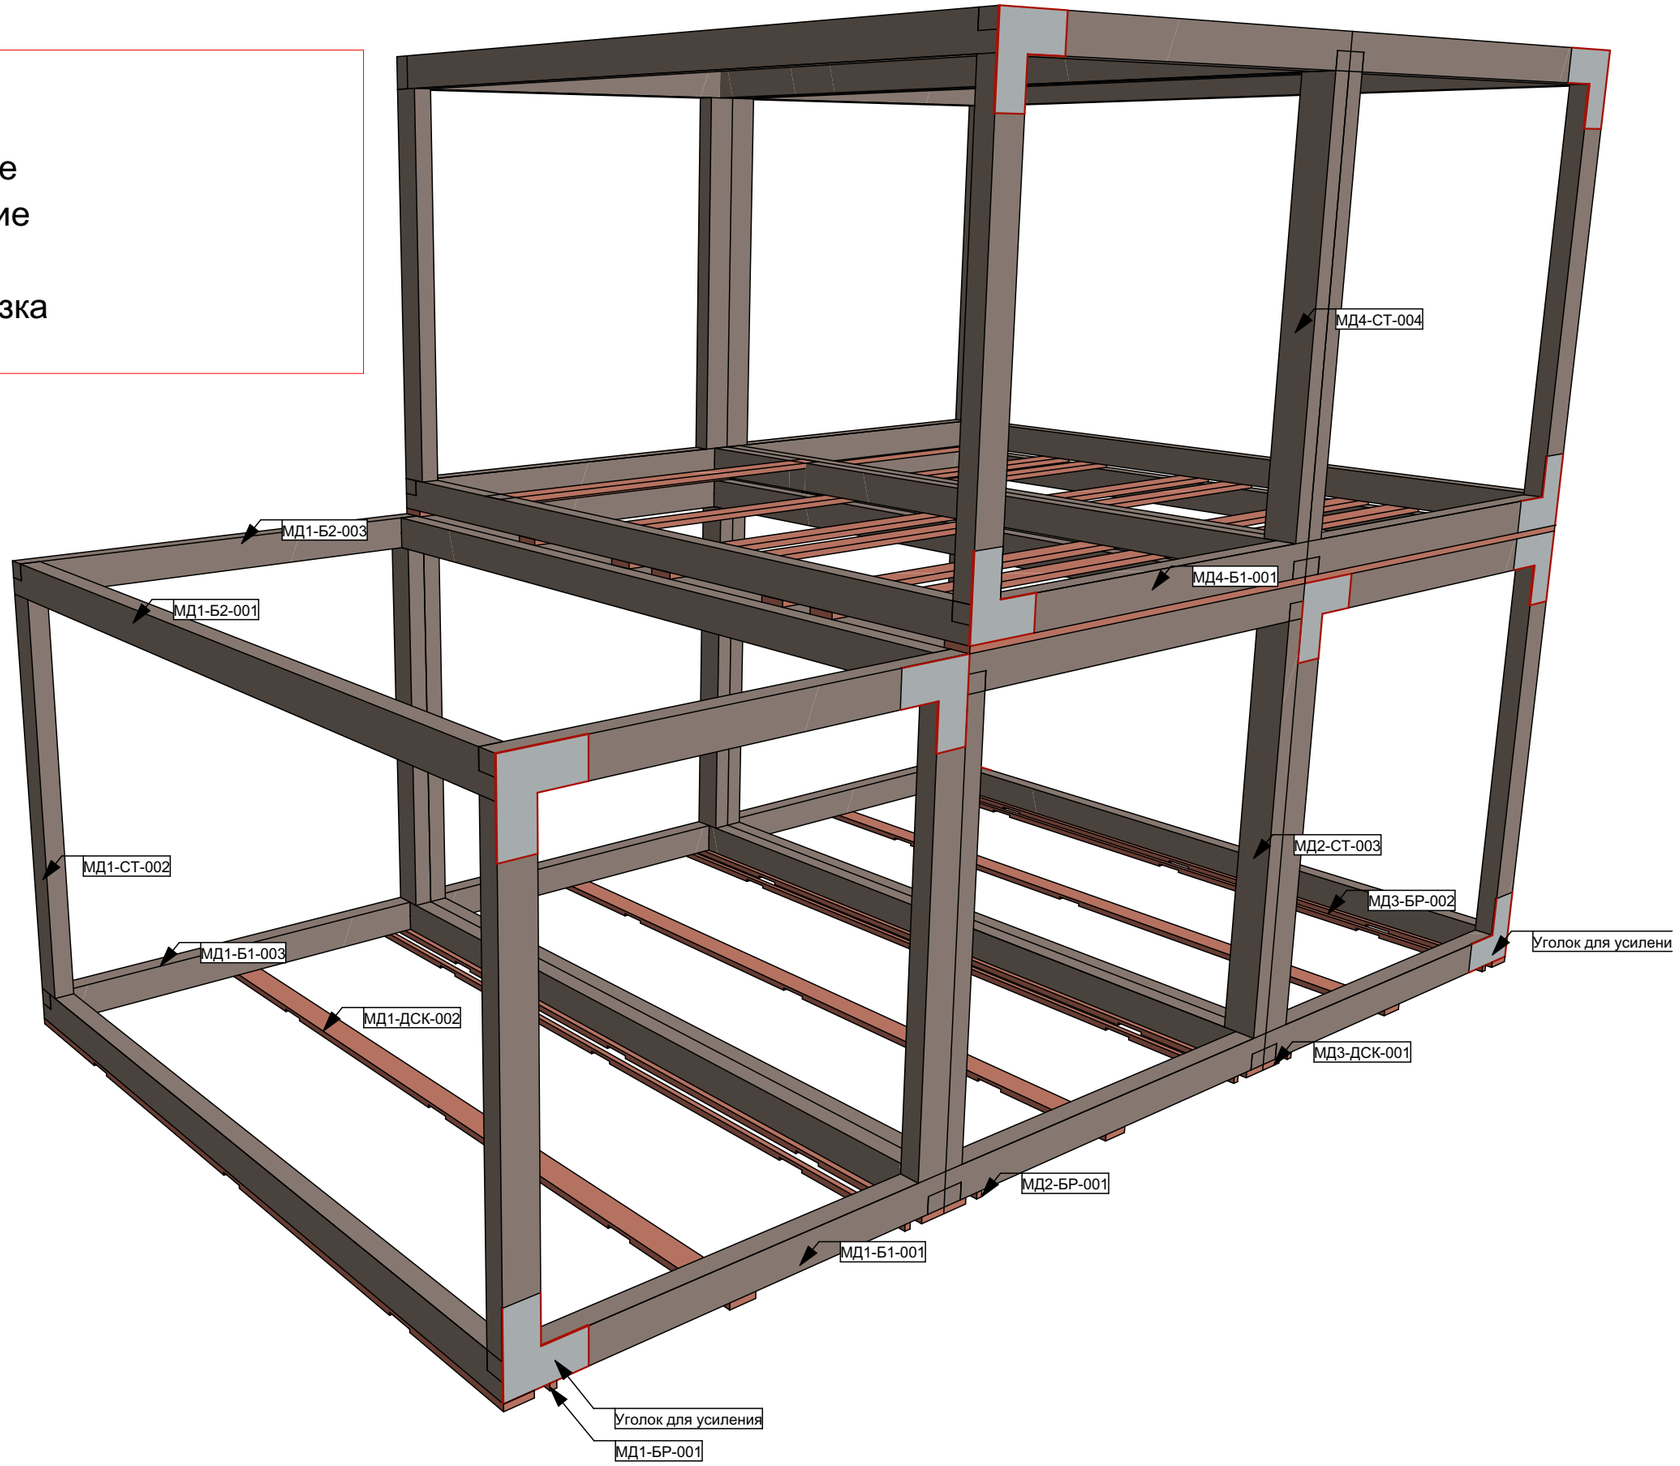

Пиломатериал	Количество
145х240	
3000	20
3280	20
6000	20
45х195	
3280	16
6000	9
45х45	
6000	6

ЛО,	...		Общий 3D Вид	Лист
Адрес строительства	Заказчик			АР1.1

ФорматА3

Жилой Дом Проба

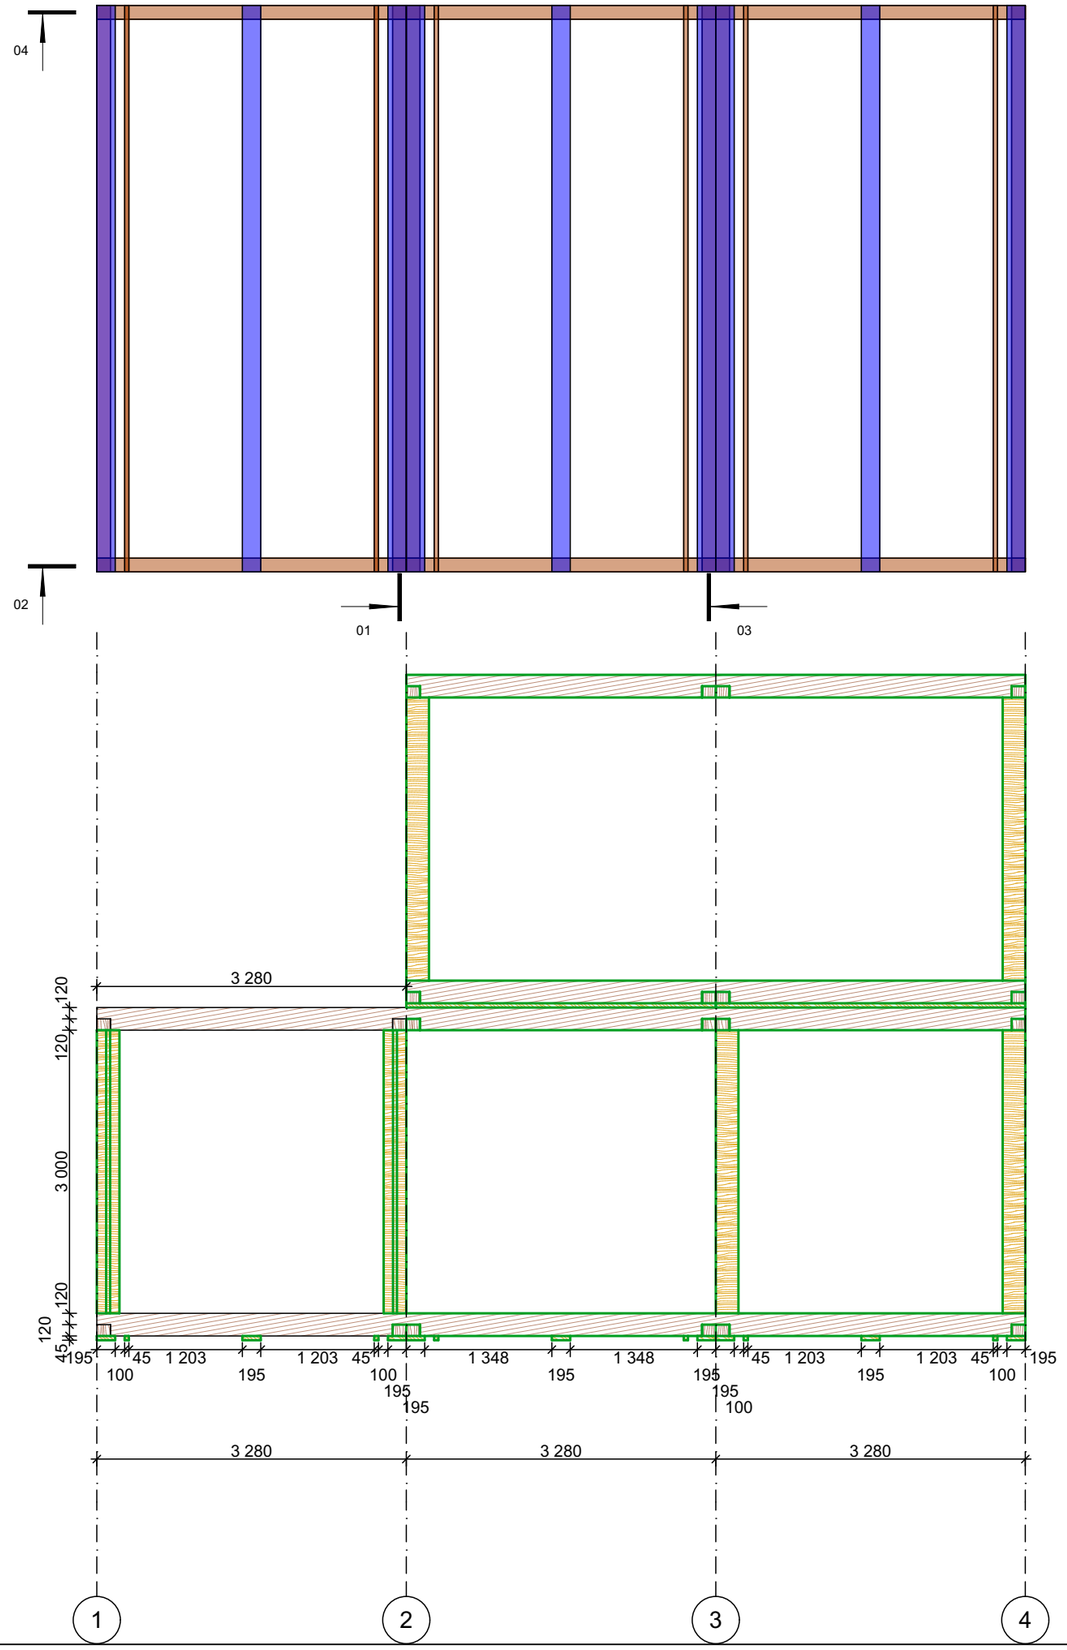

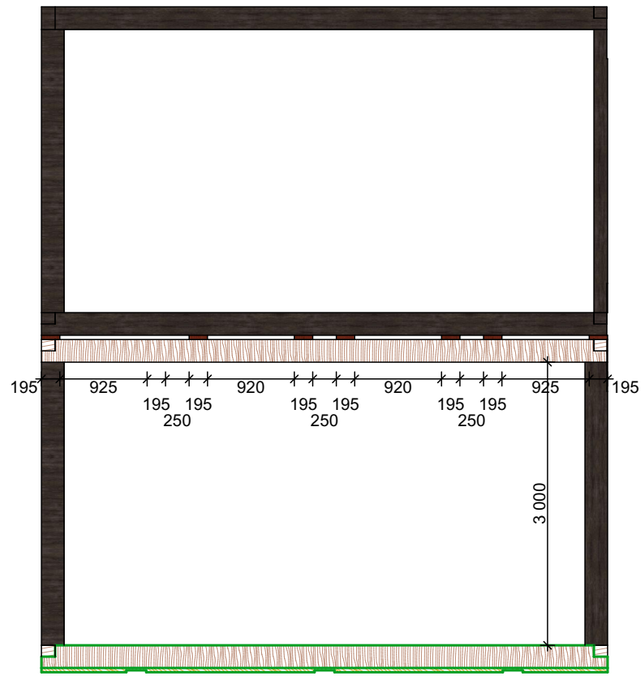

ЛО,	...		Схема сборки нижней части рам 1-й этаж	Лист
Адрес строительства	Заказчик			АР1.2

ФорматА3

Жилой Дом Проба

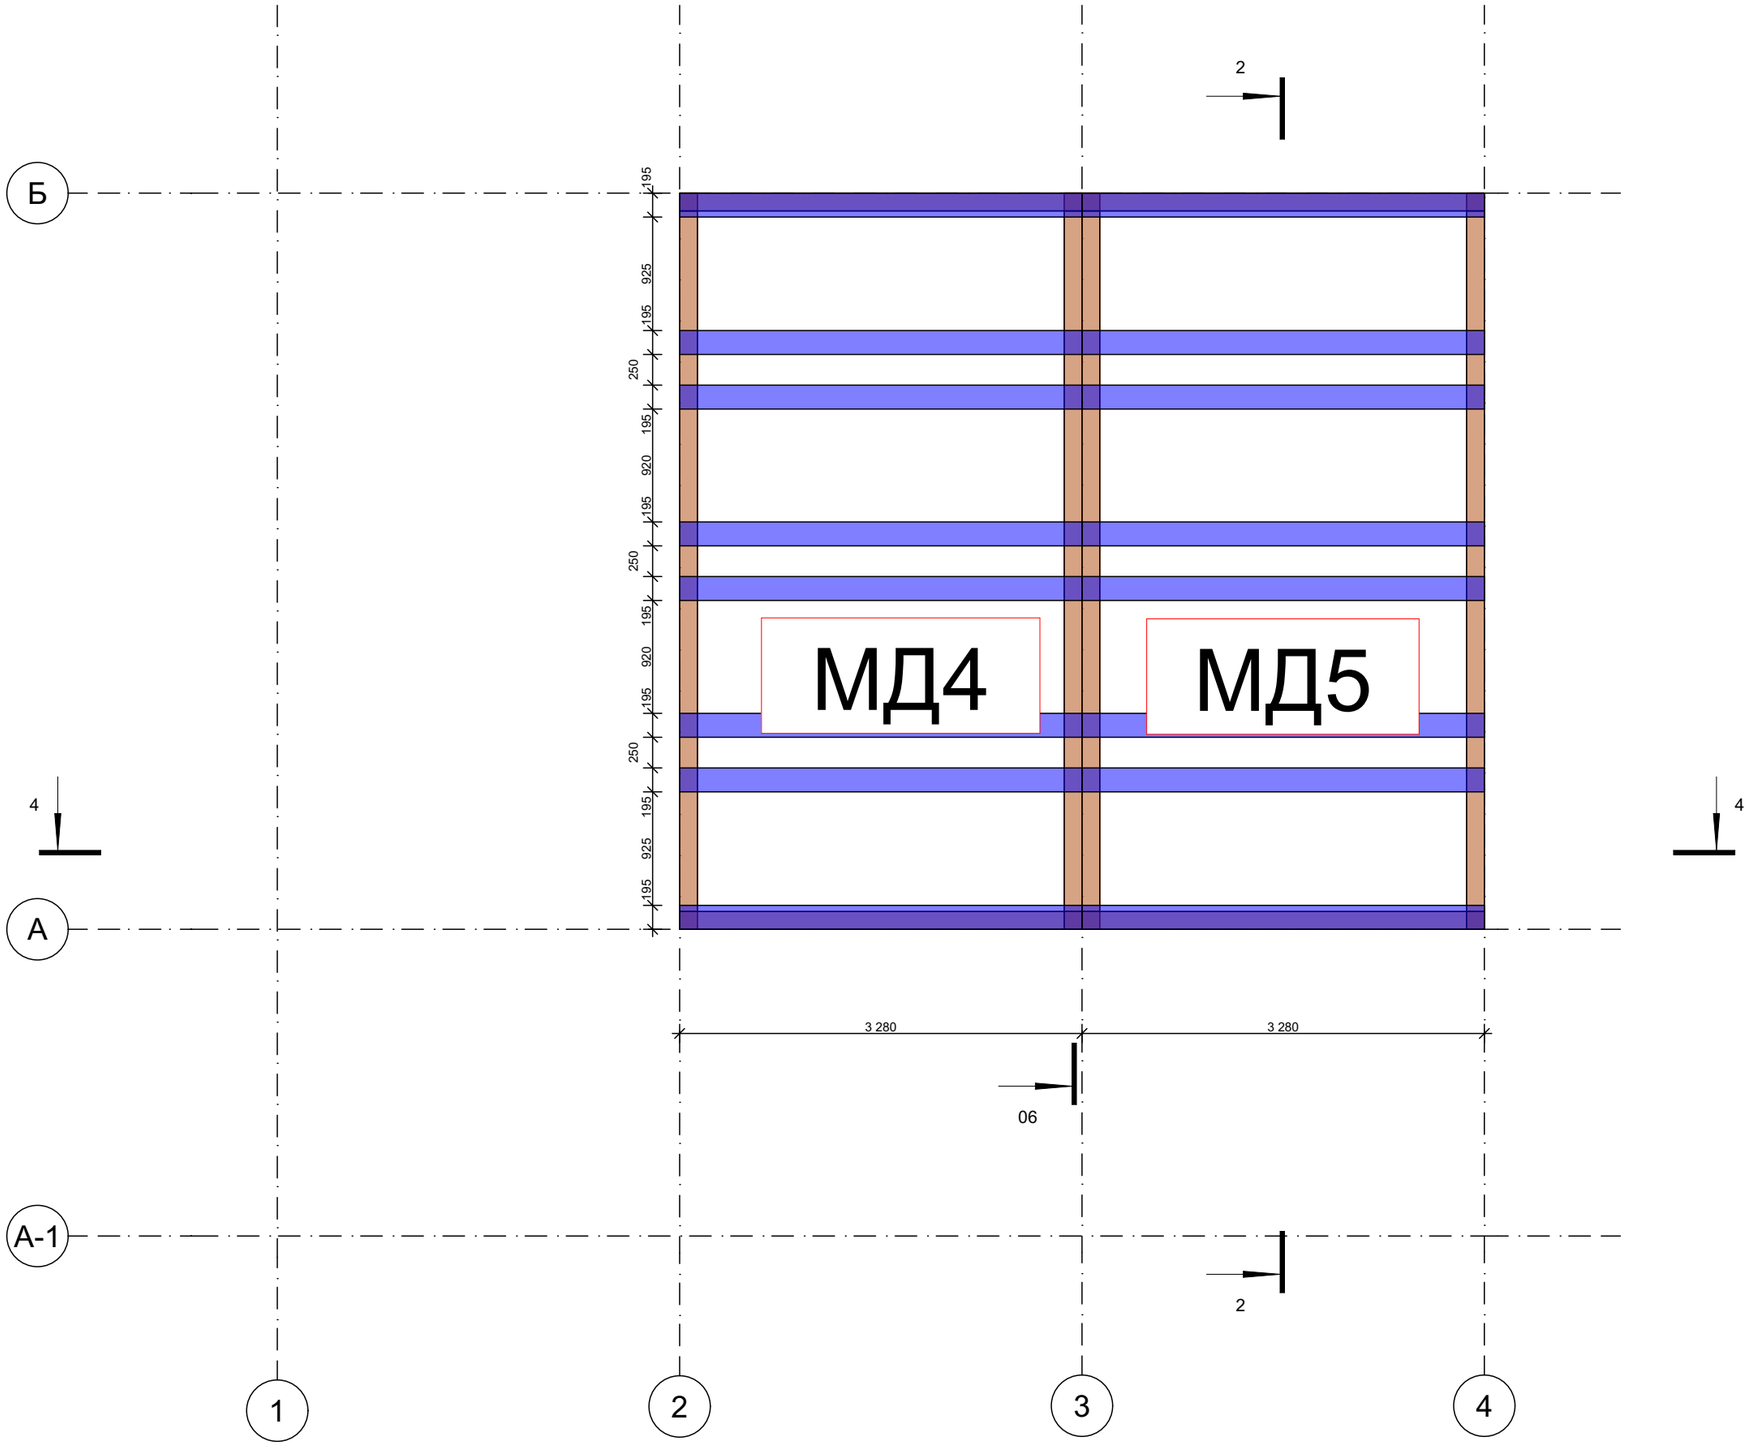

3. Перекрытие пола 2-й этаж 1:50

	ЛО,	...		Схема сборки рамы 2-й этаж	Лист
	Адрес строительства	Заказчик			АР1.3

ФорматА3

Жилой Дом Проба

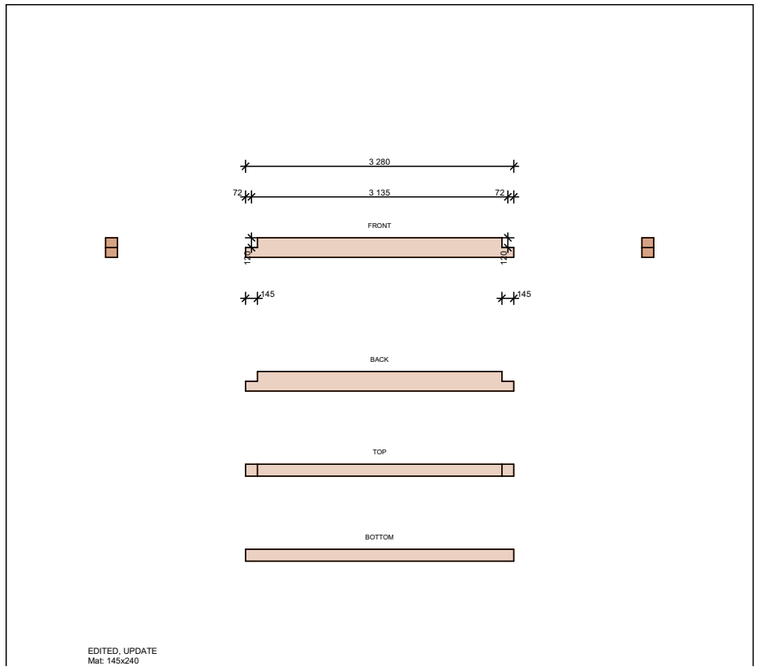

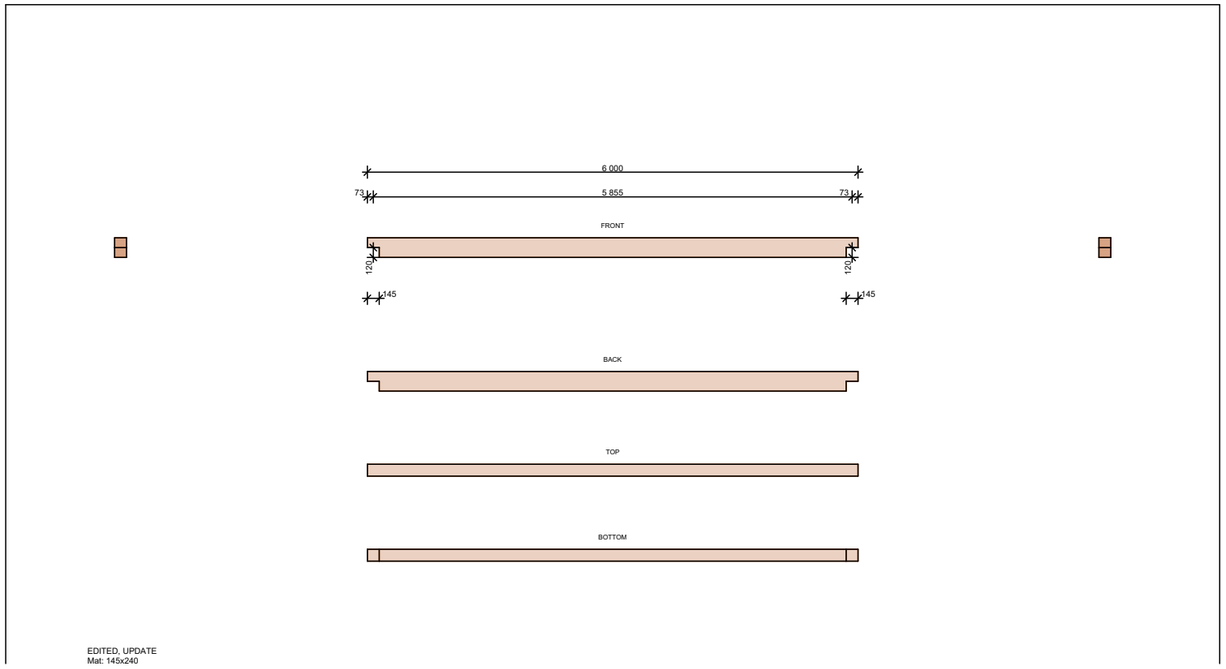

Расшифровка ID :
МД1...МД5 - номер модуля
БЛ1 - Балки горизонтальные нижние
БЛ2 - Балки горизонтальные верхние
СТ - Балки вертикальные
ДСК - Доски 45х195 под балки обвязка
БР - Брусок 45х45 под балки

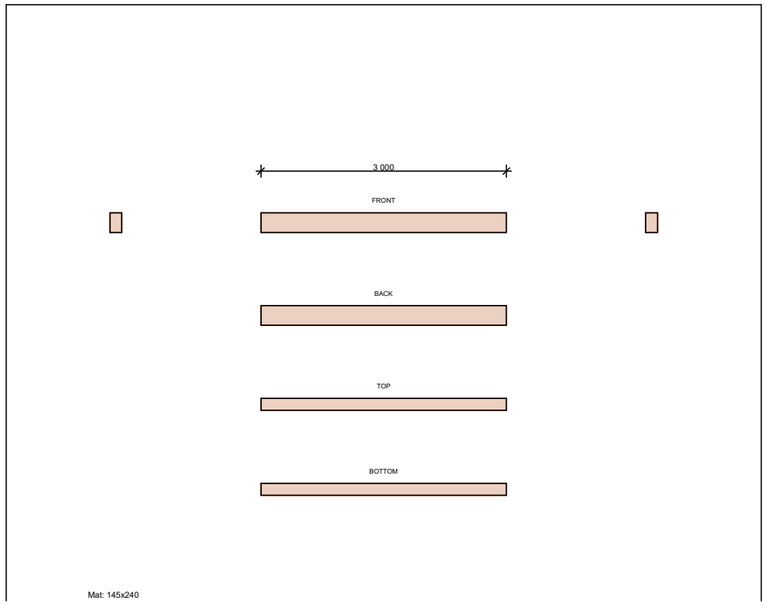

	ЛО,	...		Чертежи балок	Лист
	Адрес строительства	Заказчик			АР1.4

ФорматА3

Жилой Дом Проба

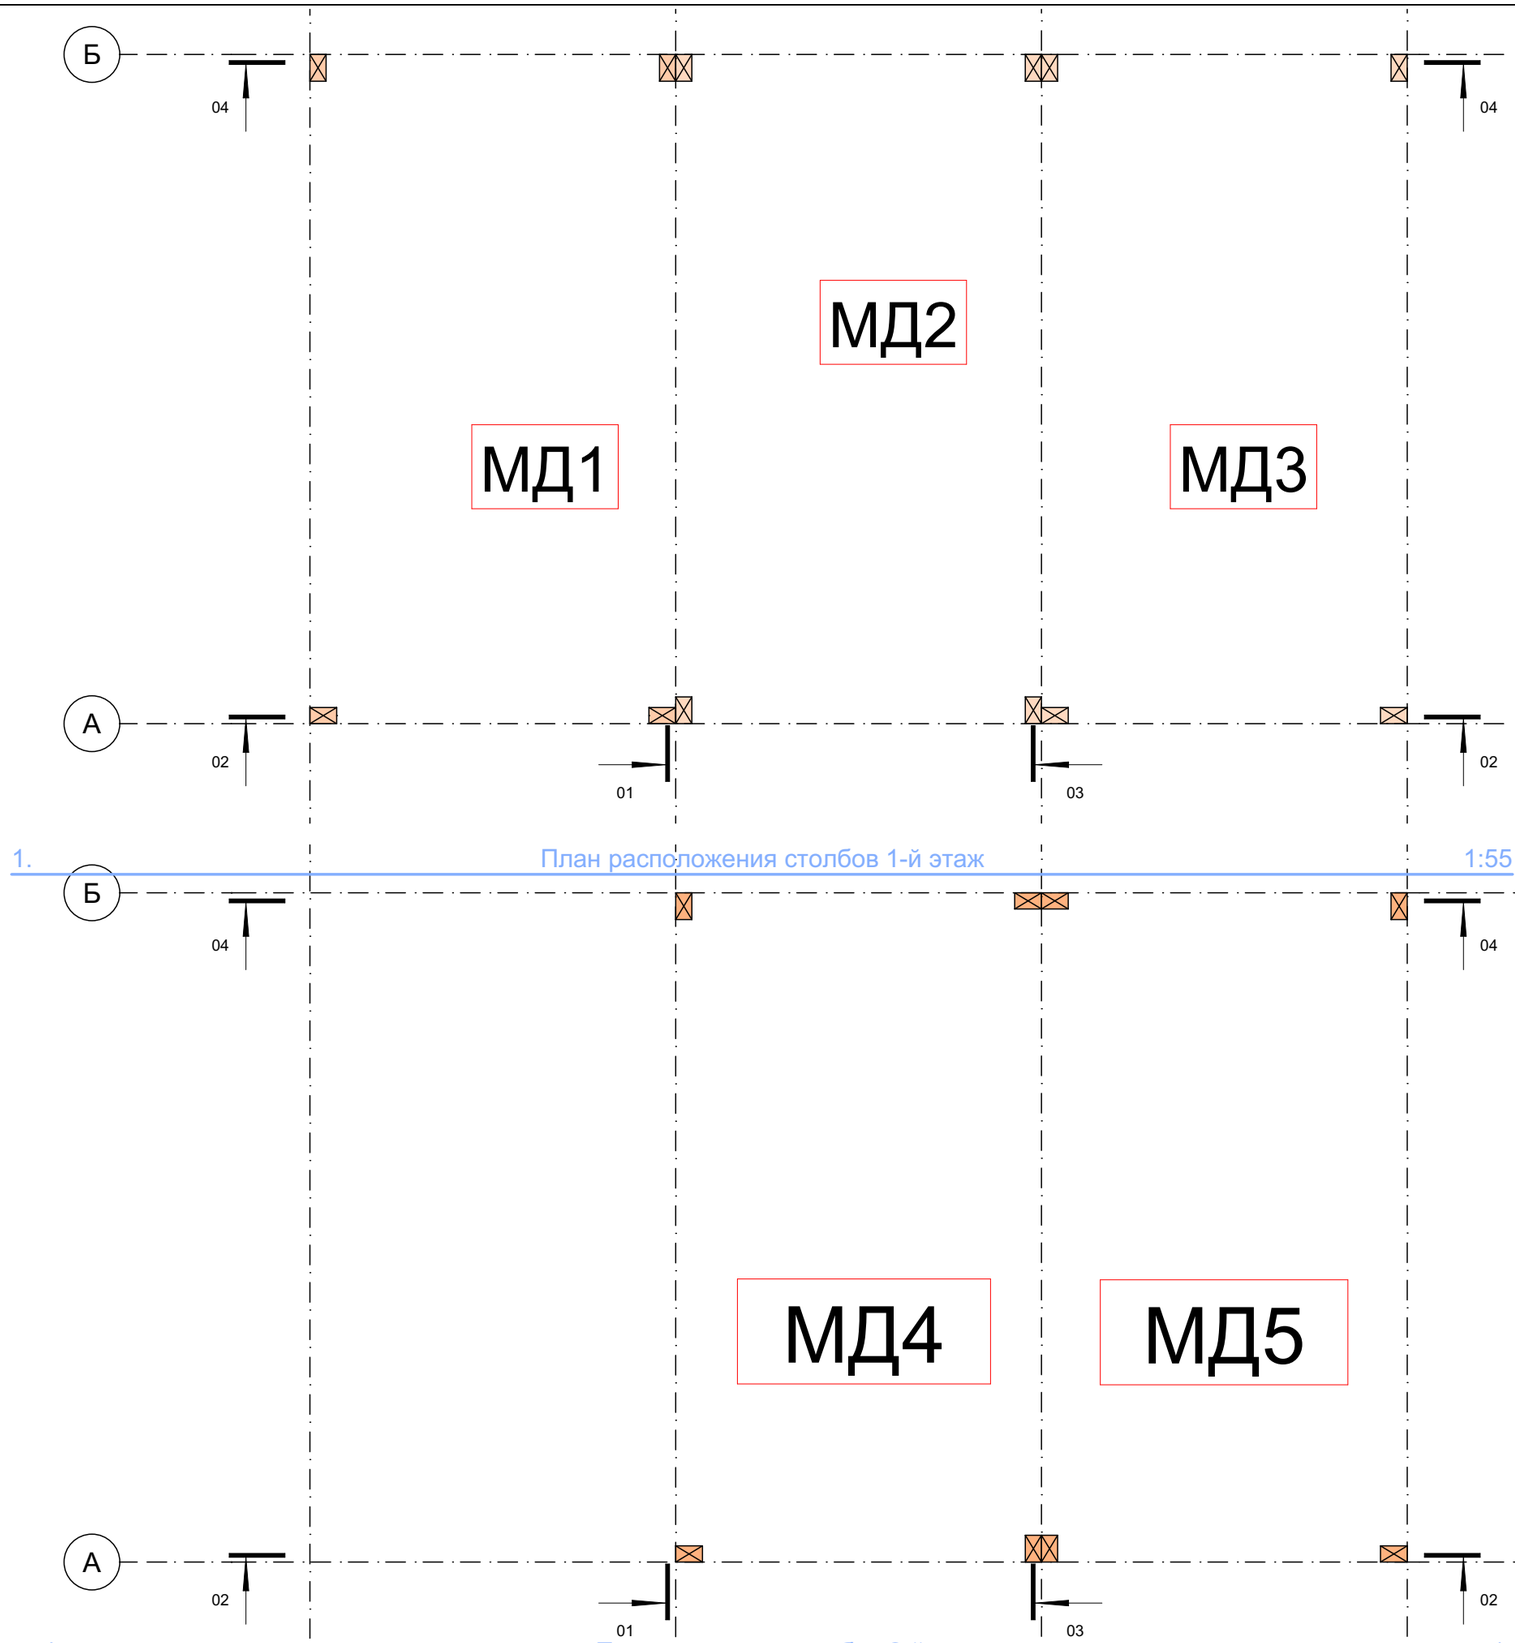

1. План расположения столбов 1-й этаж 1:55

4. План установки столбов 2-й этаж 1:55

	ЛО,	...		Схема установки столбов	Лист
	Адрес строительства	Заказчик			АР1.5

ФорматА3